

ООО «Проектный институт "Градпроект"»
Регистрационный номер в реестре членов СРО: СРО-П-088-1234 от 14.03.2019

Заказчик — ООО «Специализированный застройщик "Новый квартал"»

**МНОГОКВАРТИРНЫЙ ЖИЛОЙ ДОМ СО ВСТРОЕННЫМИ
НЕЖИЛЫМИ ПОМЕЩЕНИЯМИ ПО АДРЕСУ: МОСКОВСКАЯ
ОБЛАСТЬ, Г. О. ПОДОЛЬСК, УЛ. СТРОИТЕЛЕЙ, З/У 12**

ПРОЕКТНАЯ ДОКУМЕНТАЦИЯ
Раздел 5. Сведения об инженерном оборудовании
Подраздел 4. Отопление, вентиляция и
кондиционирование воздуха, тепловые сети

НК12-2023-ИОС4

Том 5.4

Главный инженер проекта

А. С. Петров

г. Подольск, 2023

Демонстрационный пример: объект, организации, лица и реквизиты вымышлены.

Вентиляция встроенных нежилых помещений

Из санузлов встроенных помещений предусмотрена вытяжная вентиляция с механическим побуждением: санузлы 104, 105 и 107 — система В9, санузлы 113 и 114 — система В11. Из комнаты уборочного инвентаря 106 — система В10, из помещения охраны 108 — система В12. Воздухообмен санузлов — 50 м³/ч на унитаз.

Состав систем и обслуживаемые помещения приведены на листе 2 «Характеристика отопительно-вентиляционных систем», размещение решёток — на листе 3 «План 1-го этажа. Вентиляция».

Демонстрационный пример: объект, организации, лица и реквизиты вымышлены.

						НК12-2023-ИОС4			
Изм.	Кол.уч.	Лист	№ док.	Подп.	Дата	Отопление, вентиляция и кондиционирование воздуха. Текстовая часть	Стадия	Лист	Листов
Разраб.	Лебедева				10.23		П	1	3
Пров	Громов				10.23		ООО «Проектный институт "Градрпроект"»		
ГИП	Петров				10.23				
Н.контр.	Ерёмина				10.23				

Характеристика отопительно-вентиляционных систем

Встроенные нежилые помещения 1-го этажа и техническое подполье, секция 1

Обозначение системы	Кол. систем	Наименование обслуживаемого помещения	Тип установки	Вентилятор, тип	L, м³/ч	Pс, Па	N, кВт	Примечание
ПВ1	1	Офисы пом. 101, 102, 103	ПВУ-2400-Р	встроенный	2400	450	1,5	рекуператор
ПВ2	1	Офисы пом. 111, 112	ПВУ-1800-Р	встроенный	1800	400	1,1	рекуператор
В9	1	Санузлы пом. 104, 105, 107	ВКК-160	канальный	150	200	0,1	—
В10	1	Комната уборочного инвентаря пом. 106	ВКК-125	канальный	60	150	0,06	—
В11	1	Санузлы пом. 113, 114	ВКК-125	канальный	100	180	0,06	—
В12	1	Помещение охраны пом. 108	ВКК-125	канальный	90	150	0,06	—
ВЕ1	1	Венткамера пом. 012	—	—	120	—	—	естественная

Примечания


1. Вытяжные системы санузлов и комнаты уборочного инвентаря — с механическим побуждением, канальными вентиляторами в пространстве подвесного потолка; выброс — выше кровли по каналам-спутникам.
2. Приточно-вытяжные установки ПВ1, ПВ2 — с пластинчатыми рекуператорами и водяными воздухонагревателями, размещаются в венткамере технического подполья.

Демонстрационный пример: объект, организации, лица и реквизиты вымышлены.

						НК12-2023-ИОС4			
						Многоквартирный жилой дом со встроенными нежилыми помещениями по адресу: Московская область, г. о. Подольск, ул. Строителей, з/у 12			
Изм.	Кол.уч.	Лист	№ док.	Подп.	Дата				
Разраб.	Лебедева				10.23	Жилой дом. Встроенные нежилые помещения. Отопление и вентиляция	Стадия	Лист	Листов
Пров	Громов				10.23		П	2	
ГИП	Петров				10.23	Характеристика отопительно-вентиляционных систем	ООО «Проектный институт "Градпроект"»		
Н.контр.	Ерёмина				10.23				

План 1-го этажа на отм. 0,000. Вентиляция

Встроенные нежилые помещения, секция 1. М 1:100

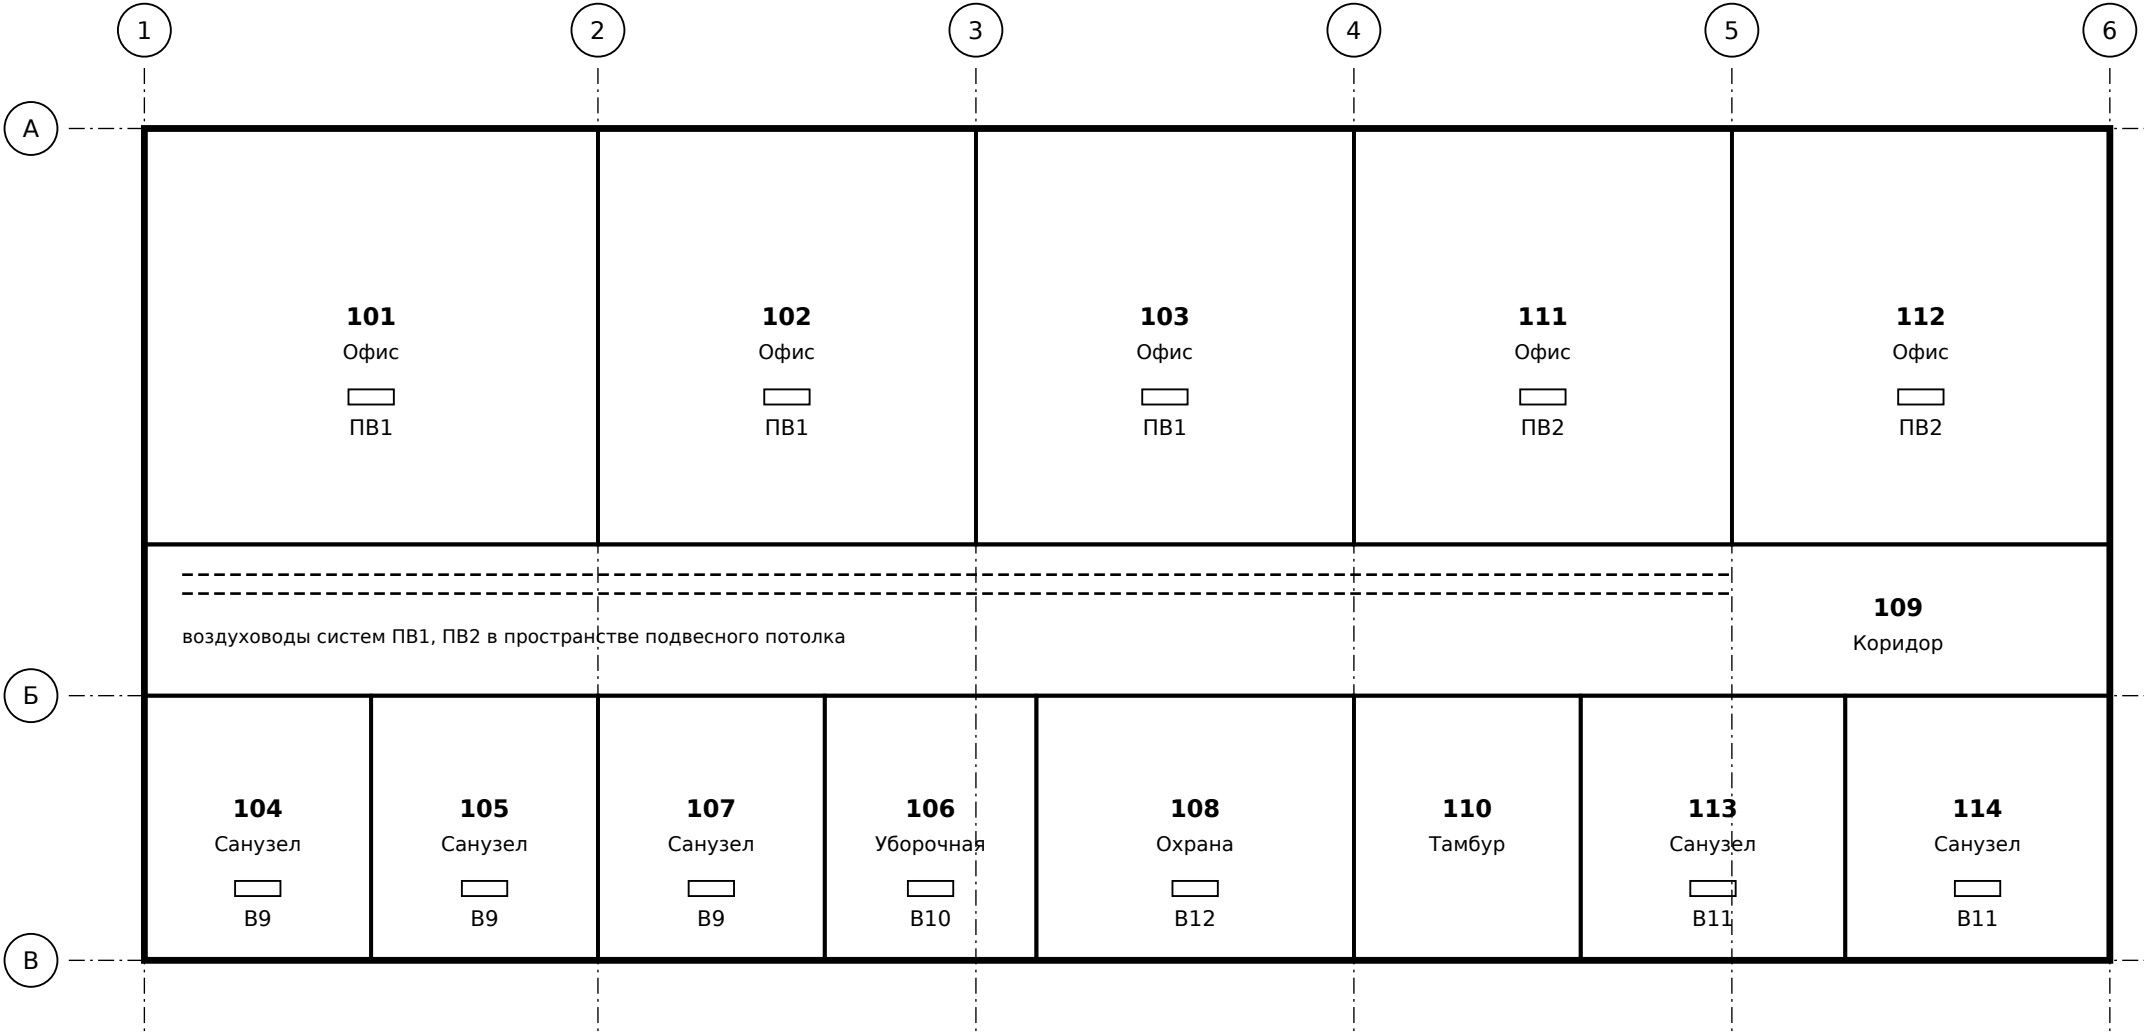

Экспликация помещений

Номер помещения	Наименование	Площадь, м²	Кат.
101	Офис	33,0	—
102	Офис	27,5	—
103	Офис	27,5	—
111	Офис	27,5	—
112	Офис	27,5	—
109	Коридор	26,0	—
104	Санузел	3,2	—
105	Санузел	3,2	—
107	Санузел	3,2	—
106	Уборочная	2,6	—
108	Охрана	8,4	—
110	Тамбур	5,1	—
113	Санузел	3,6	—
114	Санузел	3,6	—

Примечания

1. Вытяжные решётки санузлов, комнаты уборочного инвентаря и помещения охраны присоединяются к канальным вентиляторам в пространстве подвесного потолка.
2. Марки систем — по листу «Характеристика отопительно-вентиляционных систем».

Демонстрационный пример: объект, организации, лица и реквизиты вымышлены.

						НК12-2023-ИОС4			
						Многоквартирный жилой дом со встроенными нежилыми помещениями по адресу: Московская область, г. о. Подольск, ул. Строителей, з/у 12			
Изм.	Кол.уч.	Лист	№ док.	Подп.	Дата				
Разраб.	Лебедева				10.23	Жилой дом. Встроенные нежилые помещения. Отопление и вентиляция	Стадия	Лист	Листов
Пров	Громов				10.23		П	3	
ГИП	Петров				10.23	План 1-го этажа. Вентиляция	ООО «Проектный институт "Градпроект"»		
Н.контр.	Ерёмина				10.23				