

Ведомость рабочих чертежей основного комплекта

Лист	Наименование	Примечание
1	Общие данные	—
2	Фундаментная плита Фм-1. Опалубочный план. Разрез 1-1	верх плиты -2,700

Ведомость ссылочных и прилагаемых документов


Обозначение	Наименование
ГОСТ Р 21.101-2020	СПДС. Основные требования к проектной и рабочей документации
ГОСТ 21.501-2018	СПДС. Правила выполнения рабочей документации архитектурных и конструктивных решений
ГОСТ 26633-2015	Бетоны тяжёлые и мелкозернистые. Технические условия
ГОСТ 34028-2016	Прокат арматурный для железобетонных конструкций. Технические условия

Общие указания


1. Рабочая документация разработана на основании проектной документации НК12-2023-КР, получившей положительное заключение экспертизы, и задания на проектирование.
2. За относительную отметку 0,000 принят уровень чистого пола первого этажа, что соответствует абсолютной отметке 166,900.
3. Фундаментная плита Фм-1 — монолитная железобетонная толщиной 800 мм из бетона класса В25 W8 F150 по ГОСТ 26633-2015, рабочая арматура класса А500С по ГОСТ 34028-2016.
4. Наружные стены технического подполья толщиной 250 мм — из бетона класса В30 W8 F150; внутренние стены технического подполья толщиной 200 мм — из бетона класса В25 W4 F75; рабочая арматура стен — класса А500С.
5. Плита перекрытия технического подполья толщиной 200 мм — из бетона класса В25 W4 F75, рабочая арматура класса А500С.
6. Конструктивная и монтажная арматура — класса А240 по ГОСТ 34028-2016.
7. Защитный слой бетона до нижней рабочей арматуры фундаментной плиты — 40 мм, до верхней — 30 мм.
8. Бетонирование плиты вести захватками с устройством рабочих швов по узлам листа 2; уход за бетоном — по СП 70.13330.2012.
9. Освидетельствованию с составлением актов подлежат: армирование фундаментной плиты (АОСР), фундаментная плита в целом (акт освидетельствования ответственных конструкций).

						НК12-2023-КЖ1				
						Многоквартирный жилой дом со встроенными нежилыми помещениями по адресу: Московская область, г. о. Подольск, ул. Строителей, 3/у 12				
Изм.	Кол.уч.	Лист	№ док.	Подп.	Дата					
Разраб.	Волкова				10.23	Жилой дом. Конструкции железобетонные. Подземная часть		Стадия	Лист	Листов
Пров	Соколов				10.23			Р	1	2
ГИП	Петров				10.23	Общие данные		ООО «Проектный институт "Градпроект"»		
Н.контр.	Ерёмина				10.23					

Фундаментная плита Фм-1. Опалубочный план

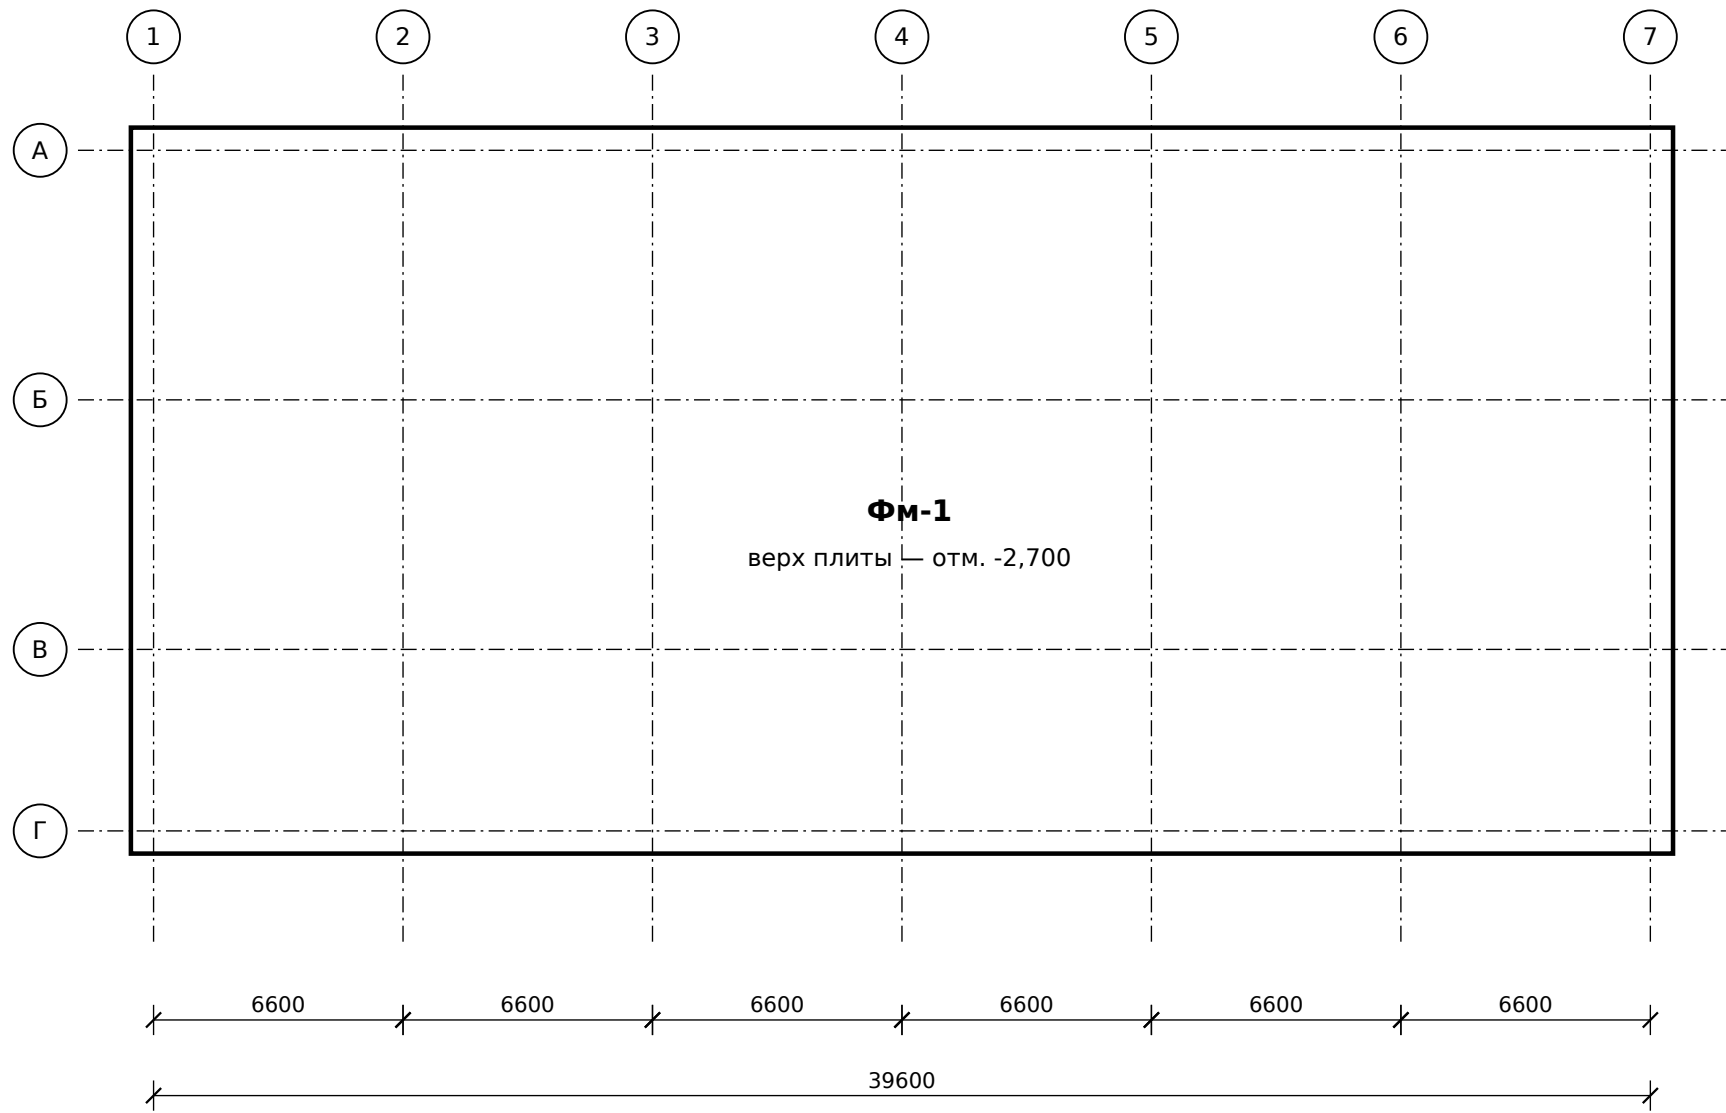

Разрез 1-1

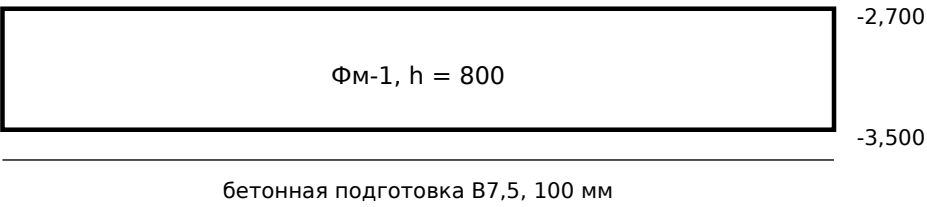

Примечания

- 1. Фундаментная плита Фм-1 толщиной 800 мм из бетона класса В25 W8 F150.
- 2. Армирование плиты — рабочая арматура класса А500С по ГОСТ 34028-2016.
- 3. Рабочие швы бетонирования — по границам захваток, с гидрошпонками.
- 4. Общие указания — см. лист 1.

Демонстрационный пример: объект, организации, лица и реквизиты вымышлены.

						НК12-2023-КЖ1			
						Многоквартирный жилой дом со встроенными нежилыми помещениями по адресу: Московская область, г. о. Подольск, ул. Строителей, з/у 12			
Изм.	Кол.уч.	Лист	№ док.	Подп.	Дата				
Разраб.	Волкова				10.23	Жилой дом. Конструкции железобетонные. Подземная часть	Стадия	Лист	Листов
Пров.	Соколов				10.23		Р	2	
ГИП	Петров				10.23	Фундаментная плита Фм-1. Опалубочный план. Разрез 1-1	ООО «Проектный институт "Градпроект"»		
Н.контр.	Ерёмина			10.23					