

Ведомость рабочих чертежей основного комплекта

Лист	Наименование	Примечание
1	Общие данные	—
2	Плита перекрытия типового этажа Пм-1. Опалубочный план	бетон В25

Ведомость ссылочных и прилагаемых документов

Обозначение	Наименование
ГОСТ Р 21.101-2020	СПДС. Основные требования к проектной и рабочей документации
ГОСТ 21.501-2018	СПДС. Правила выполнения рабочей документации архитектурных и конструктивных решений
ГОСТ 26633-2015	Бетоны тяжёлые и мелкозернистые. Технические условия
ГОСТ 34028-2016	Прокат арматурный для железобетонных конструкций. Технические условия


Общие указания

- Рабочая документация разработана на основании проектной документации НК12-2023-КР, получившей положительное заключение экспертизы.
- Стены и пилоны надземной части толщиной 200 мм — из бетона класса В25 W4 F75, рабочая арматура класса А500С.
- Плиты перекрытий и покрытия толщиной 200 мм — из бетона класса В25 W4 F75, рабочая арматура класса А500С.
- Лестничные марши и площадки — из бетона класса В25 W4 F75, рабочая арматура класса А500С.
- Конструктивная и монтажная арматура — класса А240 по ГОСТ 34028-2016.
- Защитный слой бетона до оси рабочей арматуры плит перекрытий — не менее 30 мм (REI 120).

Демонстрационный пример: объект, организации, лица и реквизиты вымышлены.

						НК12-2023-КЖ2			
						Многоквартирный жилой дом со встроенными нежилыми помещениями по адресу: Московская область, г. о. Подольск, ул. Строителей, з/у 12			
Изм.	Кол.уч.	Лист	№ док.	Подп.	Дата				
Разраб.	Волкова				10.23	Жилой дом. Конструкции железобетонные. Надземная часть	Стадия	Лист	Листов
Пров.	Соколов				10.23		Р	1	2
ГИП	Петров				10.23	Общие данные	ООО «Проектный институт "Градпроект"»		
Н.контр.	Ерёмина				10.23				

Плита перекрытия типового этажа Пм-1. Опалубочный план

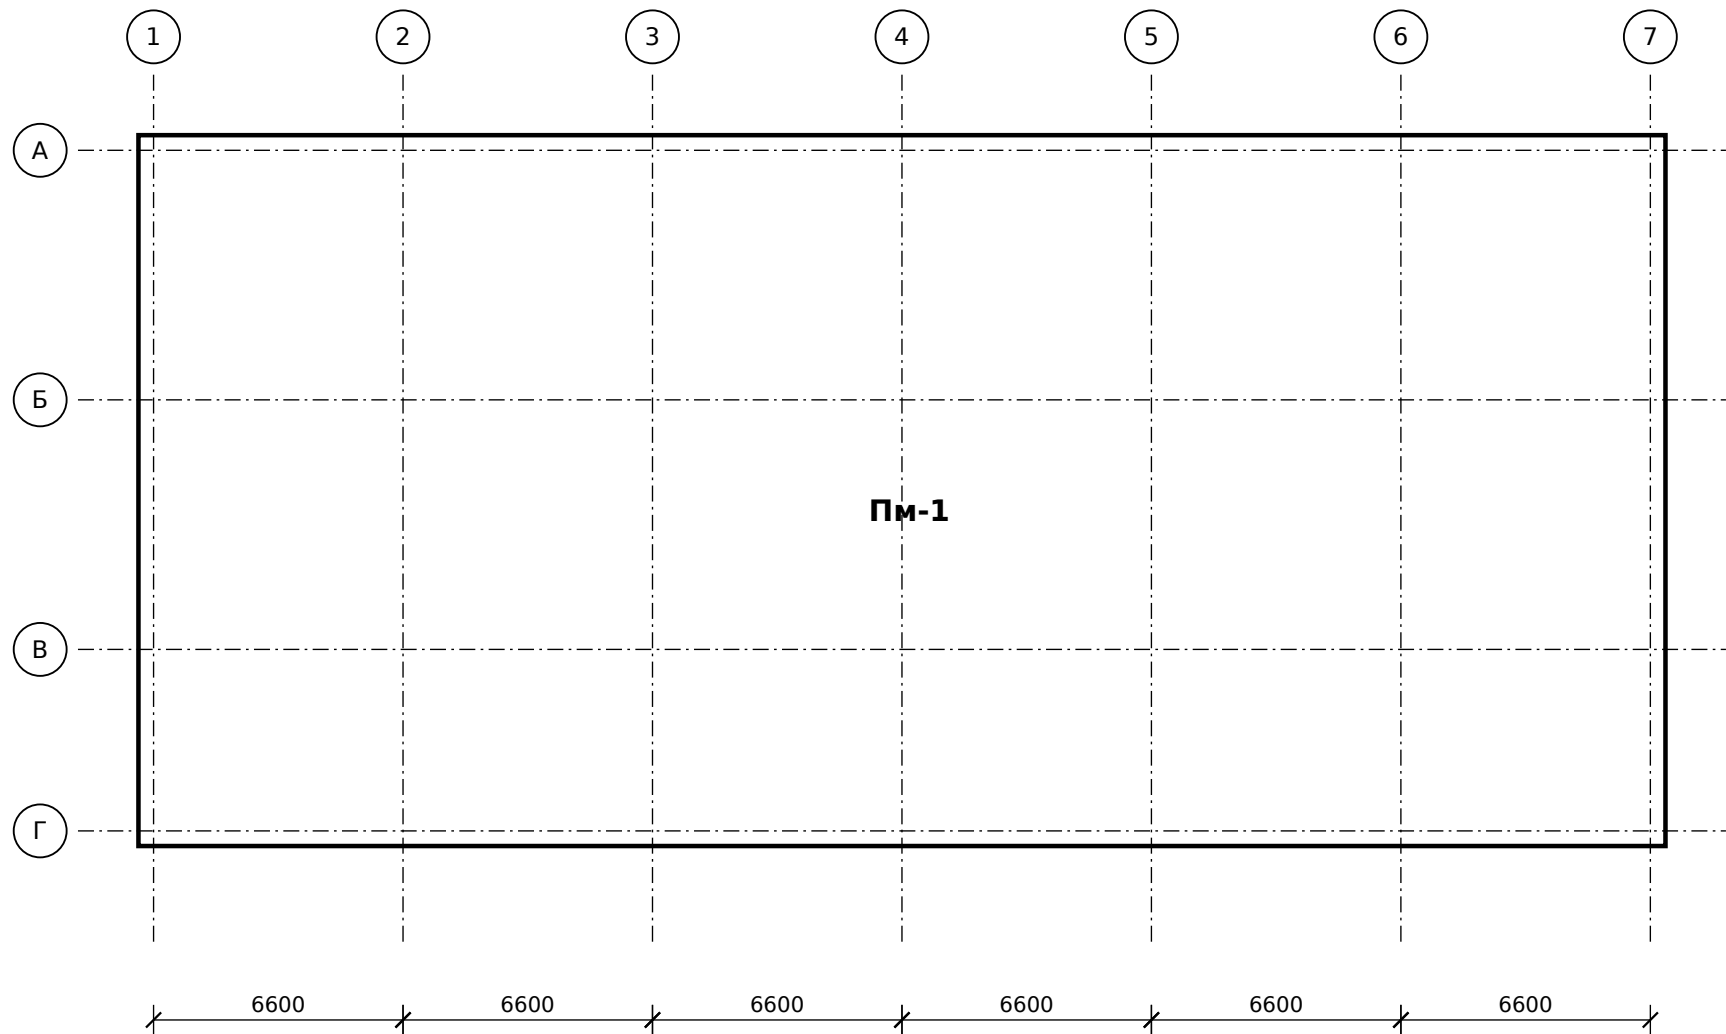

- Примечания**
- 1. Плита перекрытия Пм-1 толщиной 200 мм из бетона класса В25 W4 F75.
 - 2. Рабочая арматура класса А500С по ГОСТ 34028-2016.
 - 3. Общие указания — см. лист 1.

Демонстрационный пример: объект, организации, лица и реквизиты вымышлены.

						НК12-2023-КЖ2			
						Многоквартирный жилой дом со встроенными нежилыми помещениями по адресу: Московская область, г. о. Подольск, ул. Строителей, з/у 12			
Изм.	Кол.уч.	Лист	№ док.	Подп.	Дата				
Разраб.	Волкова				10.23	Жилой дом. Конструкции железобетонные. Надземная часть	Стадия	Лист	Листов
Пров.	Соколов				10.23		Р	2	
ГИП	Петров				10.23	Плита перекрытия типового этажа Пм-1. Опалубочный план	ООО «Проектный институт "Градпроект"»		
Н.контр.	Ерёмина				10.23				