

Ведомость рабочих чертежей основного комплекта

Лист	Наименование	Примечание
1	Общие данные	—
2	Характеристика отопительно-вентиляционных систем	встроенные помещения
3	План 1-го этажа. Вентиляция	встроенные помещения

Ведомость ссылочных и прилагаемых документов

Обозначение	Наименование
ГОСТ Р 21.101-2020	СПДС. Основные требования к проектной и рабочей документации
ГОСТ 21.602-2016	СПДС. Правила выполнения рабочей документации отопления, вентиляции и кондиционирования
СП 60.13330.2020	Отопление, вентиляция и кондиционирование воздуха

Общие указания

1. Рабочая документация разработана на основании проектной документации НК12-2023-ИОС4 и задания на проектирование.
2. Встроенные офисные помещения обслуживаются приточно-вытяжными установками ПВ1 и ПВ2 с рекуперацией.
3. Вытяжная вентиляция санузлов, комнаты уборочного инвентаря и помещения охраны — с механическим побуждением, канальными вентиляторами.
4. Воздуховоды — из тонколистовой оцинкованной стали по ГОСТ 14918-2020, класс герметичности А.
5. Монтаж и испытания систем — по СП 73.13330.2016.

						НК12-2023-ОВ			
						Многоквартирный жилой дом со встроенными нежилыми помещениями по адресу: Московская область, г. о. Подольск, ул. Строителей, з/у 12			
Изм.	Кол.уч.	Лист	№ док.	Подп.	Дата				
Разраб.	Лебедева				10.23	Жилой дом. Отопление и вентиляция	Стадия	Лист	Листов
Пров	Громов				10.23		Р	1	3
ГИП	Петров				10.23	Общие данные	ООО «Проектный институт "Градпроект"»		
Н.контр.	Ерёмина				10.23				

Характеристика отопительно-вентиляционных систем

Встроенные нежилые помещения 1-го этажа и техническое подполье, секция 1

Обозначение системы	Кол. систем	Наименование обслуживаемого помещения	Тип установки	Вентилятор, тип	L, м³/ч	Pс, Па	N, кВт	Примечание
ПВ1	1	Офисы пом. 101, 102, 103	ПВУ-2400-Р	встроенный	2400	450	1,5	рекуператор
ПВ2	1	Офисы пом. 111, 112	ПВУ-1800-Р	встроенный	1800	400	1,1	рекуператор
В9	1	Санузлы пом. 104, 105	ВКК-160	канальный	150	200	0,1	—
В10	1	Комната уборочного инвентаря пом. 106	ВКК-125	канальный	60	150	0,06	—
В11	1	Санузлы пом. 113, 114	ВКК-125	канальный	100	180	0,06	—
В12	1	Помещение охраны пом. 108	ВКК-125	канальный	90	150	0,06	—
ВЕ1	1	Венткамера пом. 012	—	—	120	—	—	естественная

Примечания


1. Вытяжные системы санузлов и комнаты уборочного инвентаря — с механическим побуждением, канальными вентиляторами в пространстве подвесного потолка; выброс — выше кровли по каналам-спутникам.
2. Приточно-вытяжные установки ПВ1, ПВ2 — с пластинчатыми рекуператорами и водяными воздухонагревателями, размещаются в венткамере технического подполья.

Демонстрационный пример: объект, организации, лица и реквизиты вымышлены.

						НК12-2023-ОВ			
						Многоквартирный жилой дом со встроенными нежилыми помещениями по адресу: Московская область, г. о. Подольск, ул. Строителей, з/у 12			
Изм.	Кол.уч.	Лист	№ док.	Подп.	Дата				
Разраб.	Лебедева				10.23	Жилой дом. Встроенные нежилые помещения. Отопление и вентиляция	Стадия	Лист	Листов
Пров	Громов				10.23		Р	2	
ГИП	Петров				10.23	Характеристика отопительно-вентиляционных систем	ООО «Проектный институт "Градпроект"»		
Н.контр.	Ерёмина				10.23				

План 1-го этажа на отм. 0,000. Вентиляция

Встроенные нежилые помещения, секция 1. М 1:100

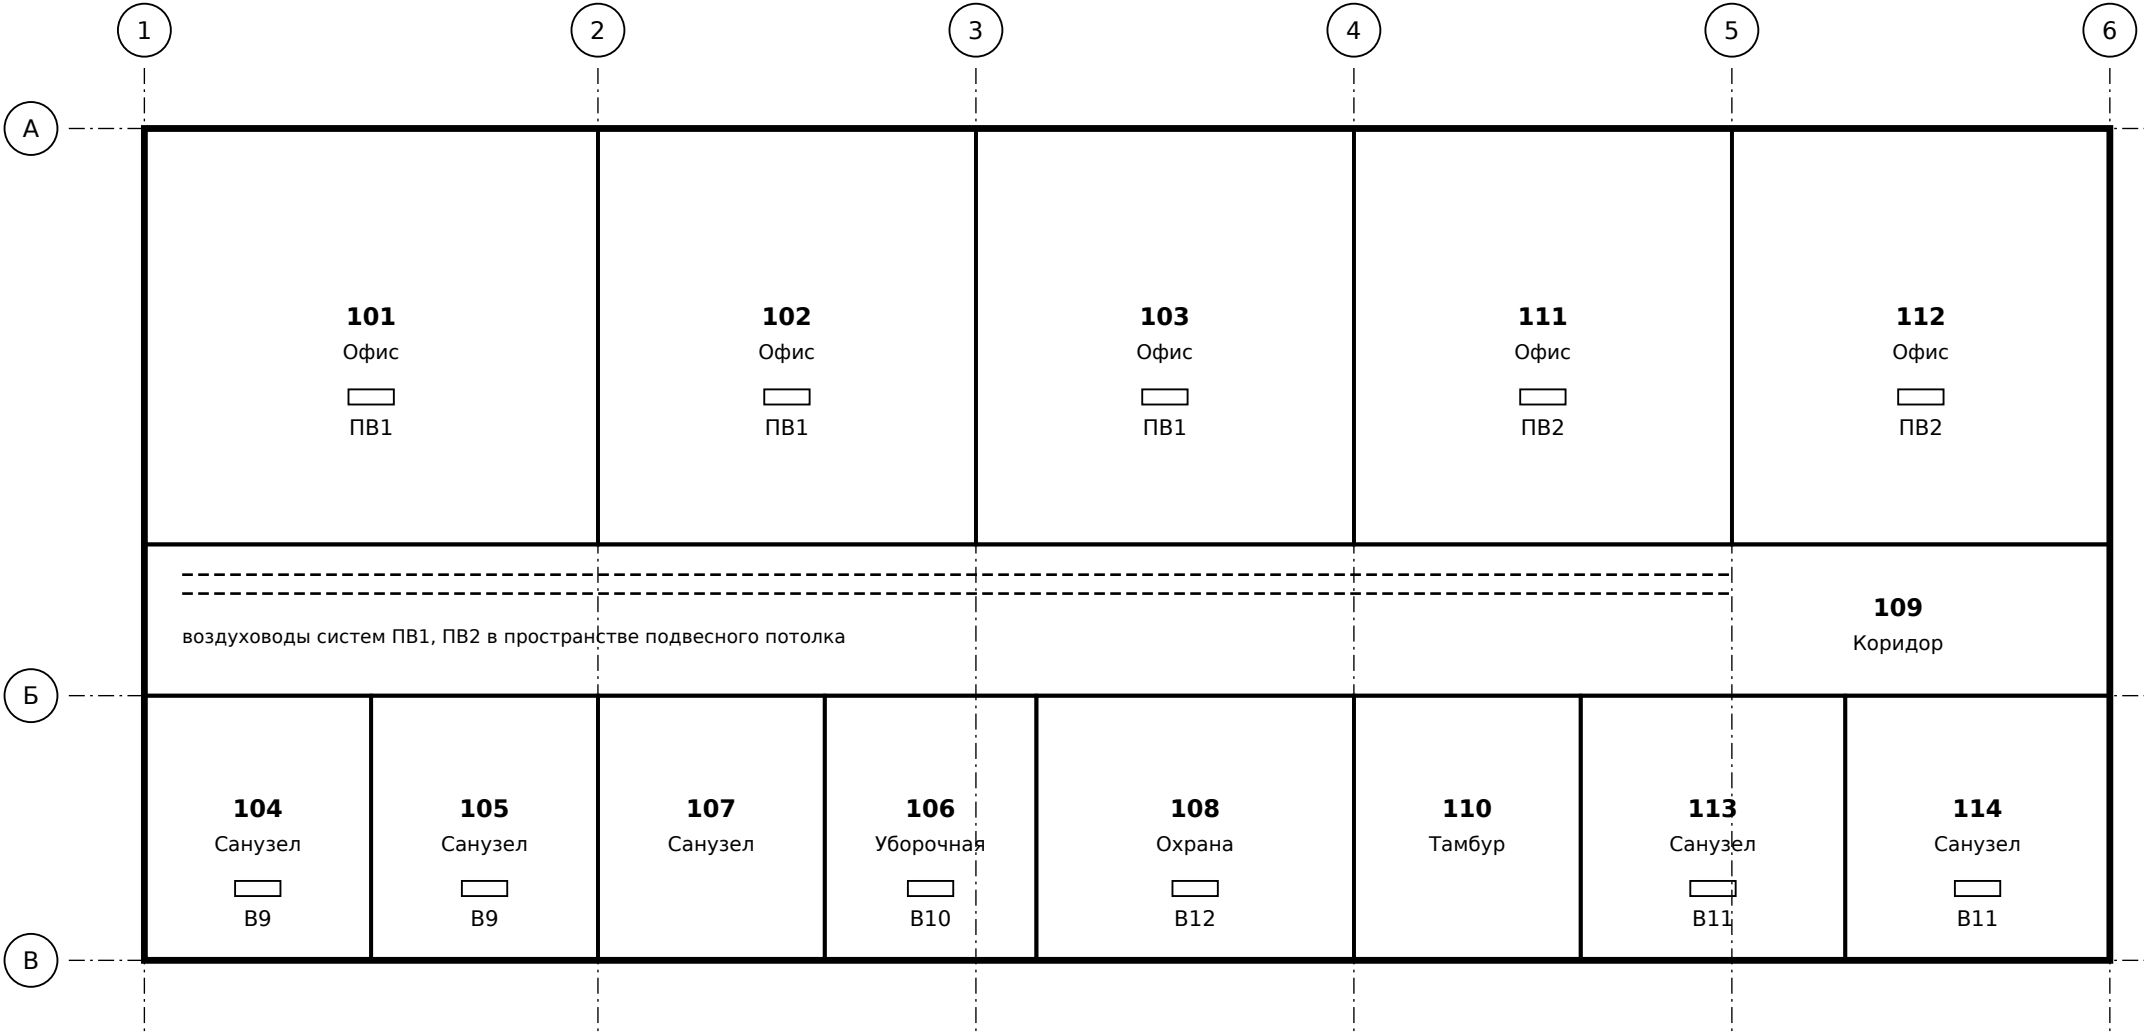

Экспликация помещений

Номер помещения	Наименование	Площадь, м²	Кат.
101	Офис	33,0	—
102	Офис	27,5	—
103	Офис	27,5	—
111	Офис	27,5	—
112	Офис	27,5	—
109	Коридор	26,0	—
104	Санузел	3,2	—
105	Санузел	3,2	—
107	Санузел	3,2	—
106	Уборочная	2,6	—
108	Охрана	8,4	—
110	Тамбур	5,1	—
113	Санузел	3,6	—
114	Санузел	3,6	—

Примечания

1. Вытяжные решётки санузлов, комнаты уборочного инвентаря и помещения охраны присоединяются к канальным вентиляторам в пространстве подвесного потолка.
2. Марки систем — по листу «Характеристика отопительно-вентиляционных систем».

Демонстрационный пример: объект, организации, лица и реквизиты вымышлены.

						НК12-2023-ОВ			
						Многоквартирный жилой дом со встроенными нежилыми помещениями по адресу: Московская область, г. о. Подольск, ул. Строителей, з/у 12			
Изм.	Кол.уч.	Лист	№ док.	Подп.	Дата				
Разраб.	Лебедева				10.23	Жилой дом. Встроенные нежилые помещения. Отопление и вентиляция	Стадия	Лист	Листов
Пров	Громов				10.23		Р	3	
ГИП	Петров				10.23	План 1-го этажа. Вентиляция	ООО «Проектный институт "Градпроект"»		
Н.контр.	Ерёмина				10.23				